
ジエスタ2防火戸／ジエスタ2（ハイサイズ仕様）アングル付　親子・両開き（横断面図）K4

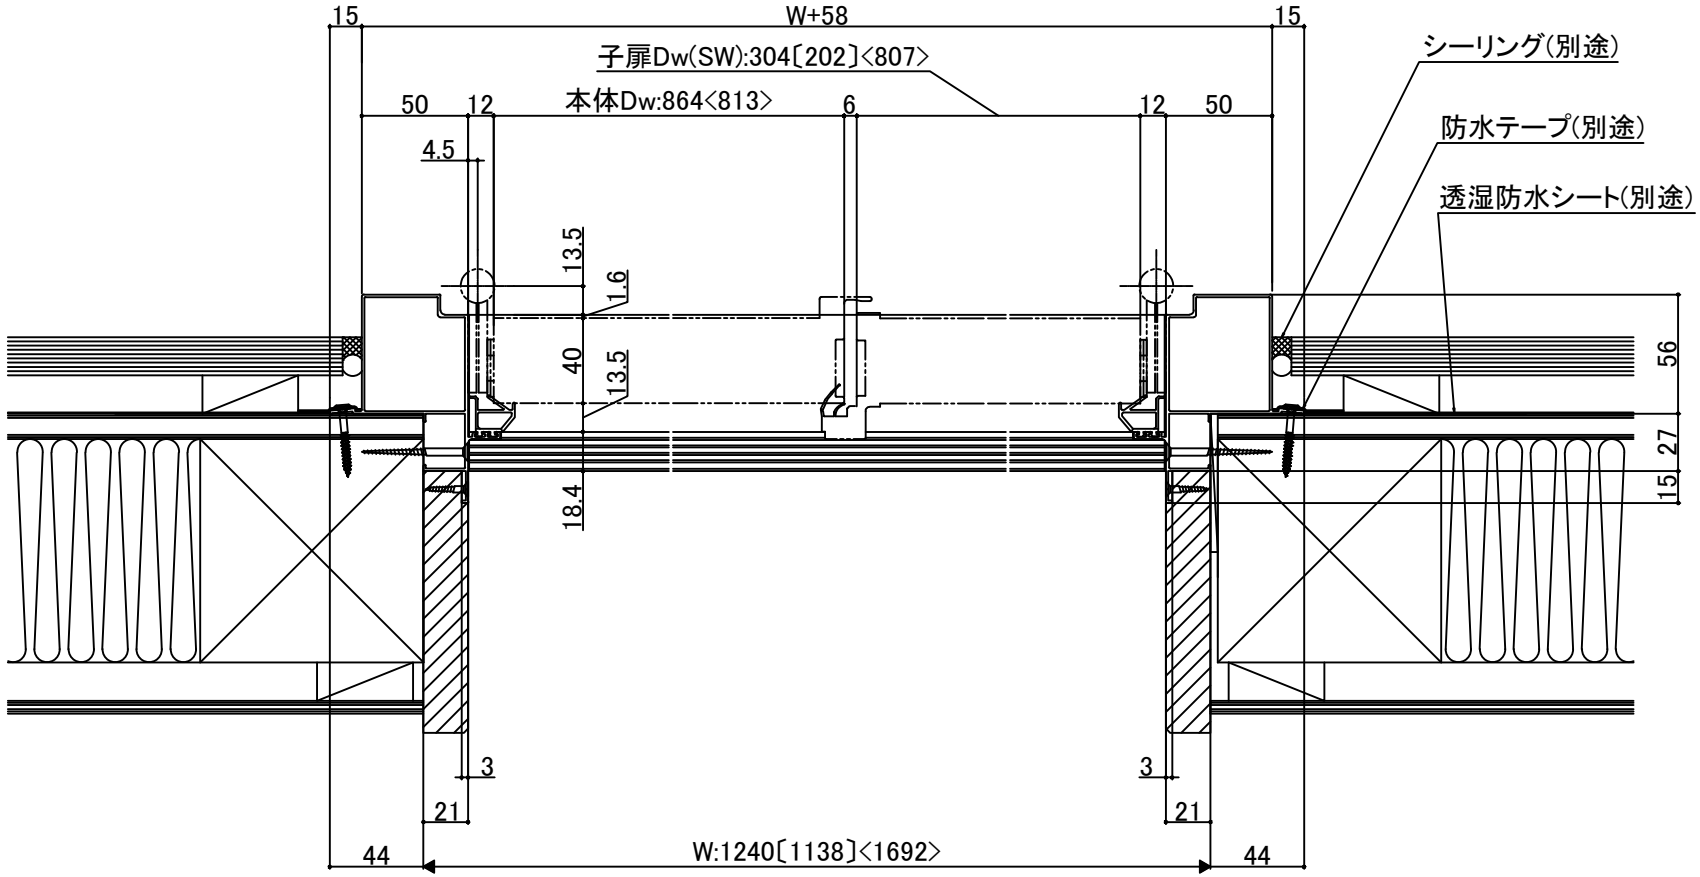

〔 〕内は入隅用寸法を示す。
< >内は両開き用寸法を示す。

H200G14005